



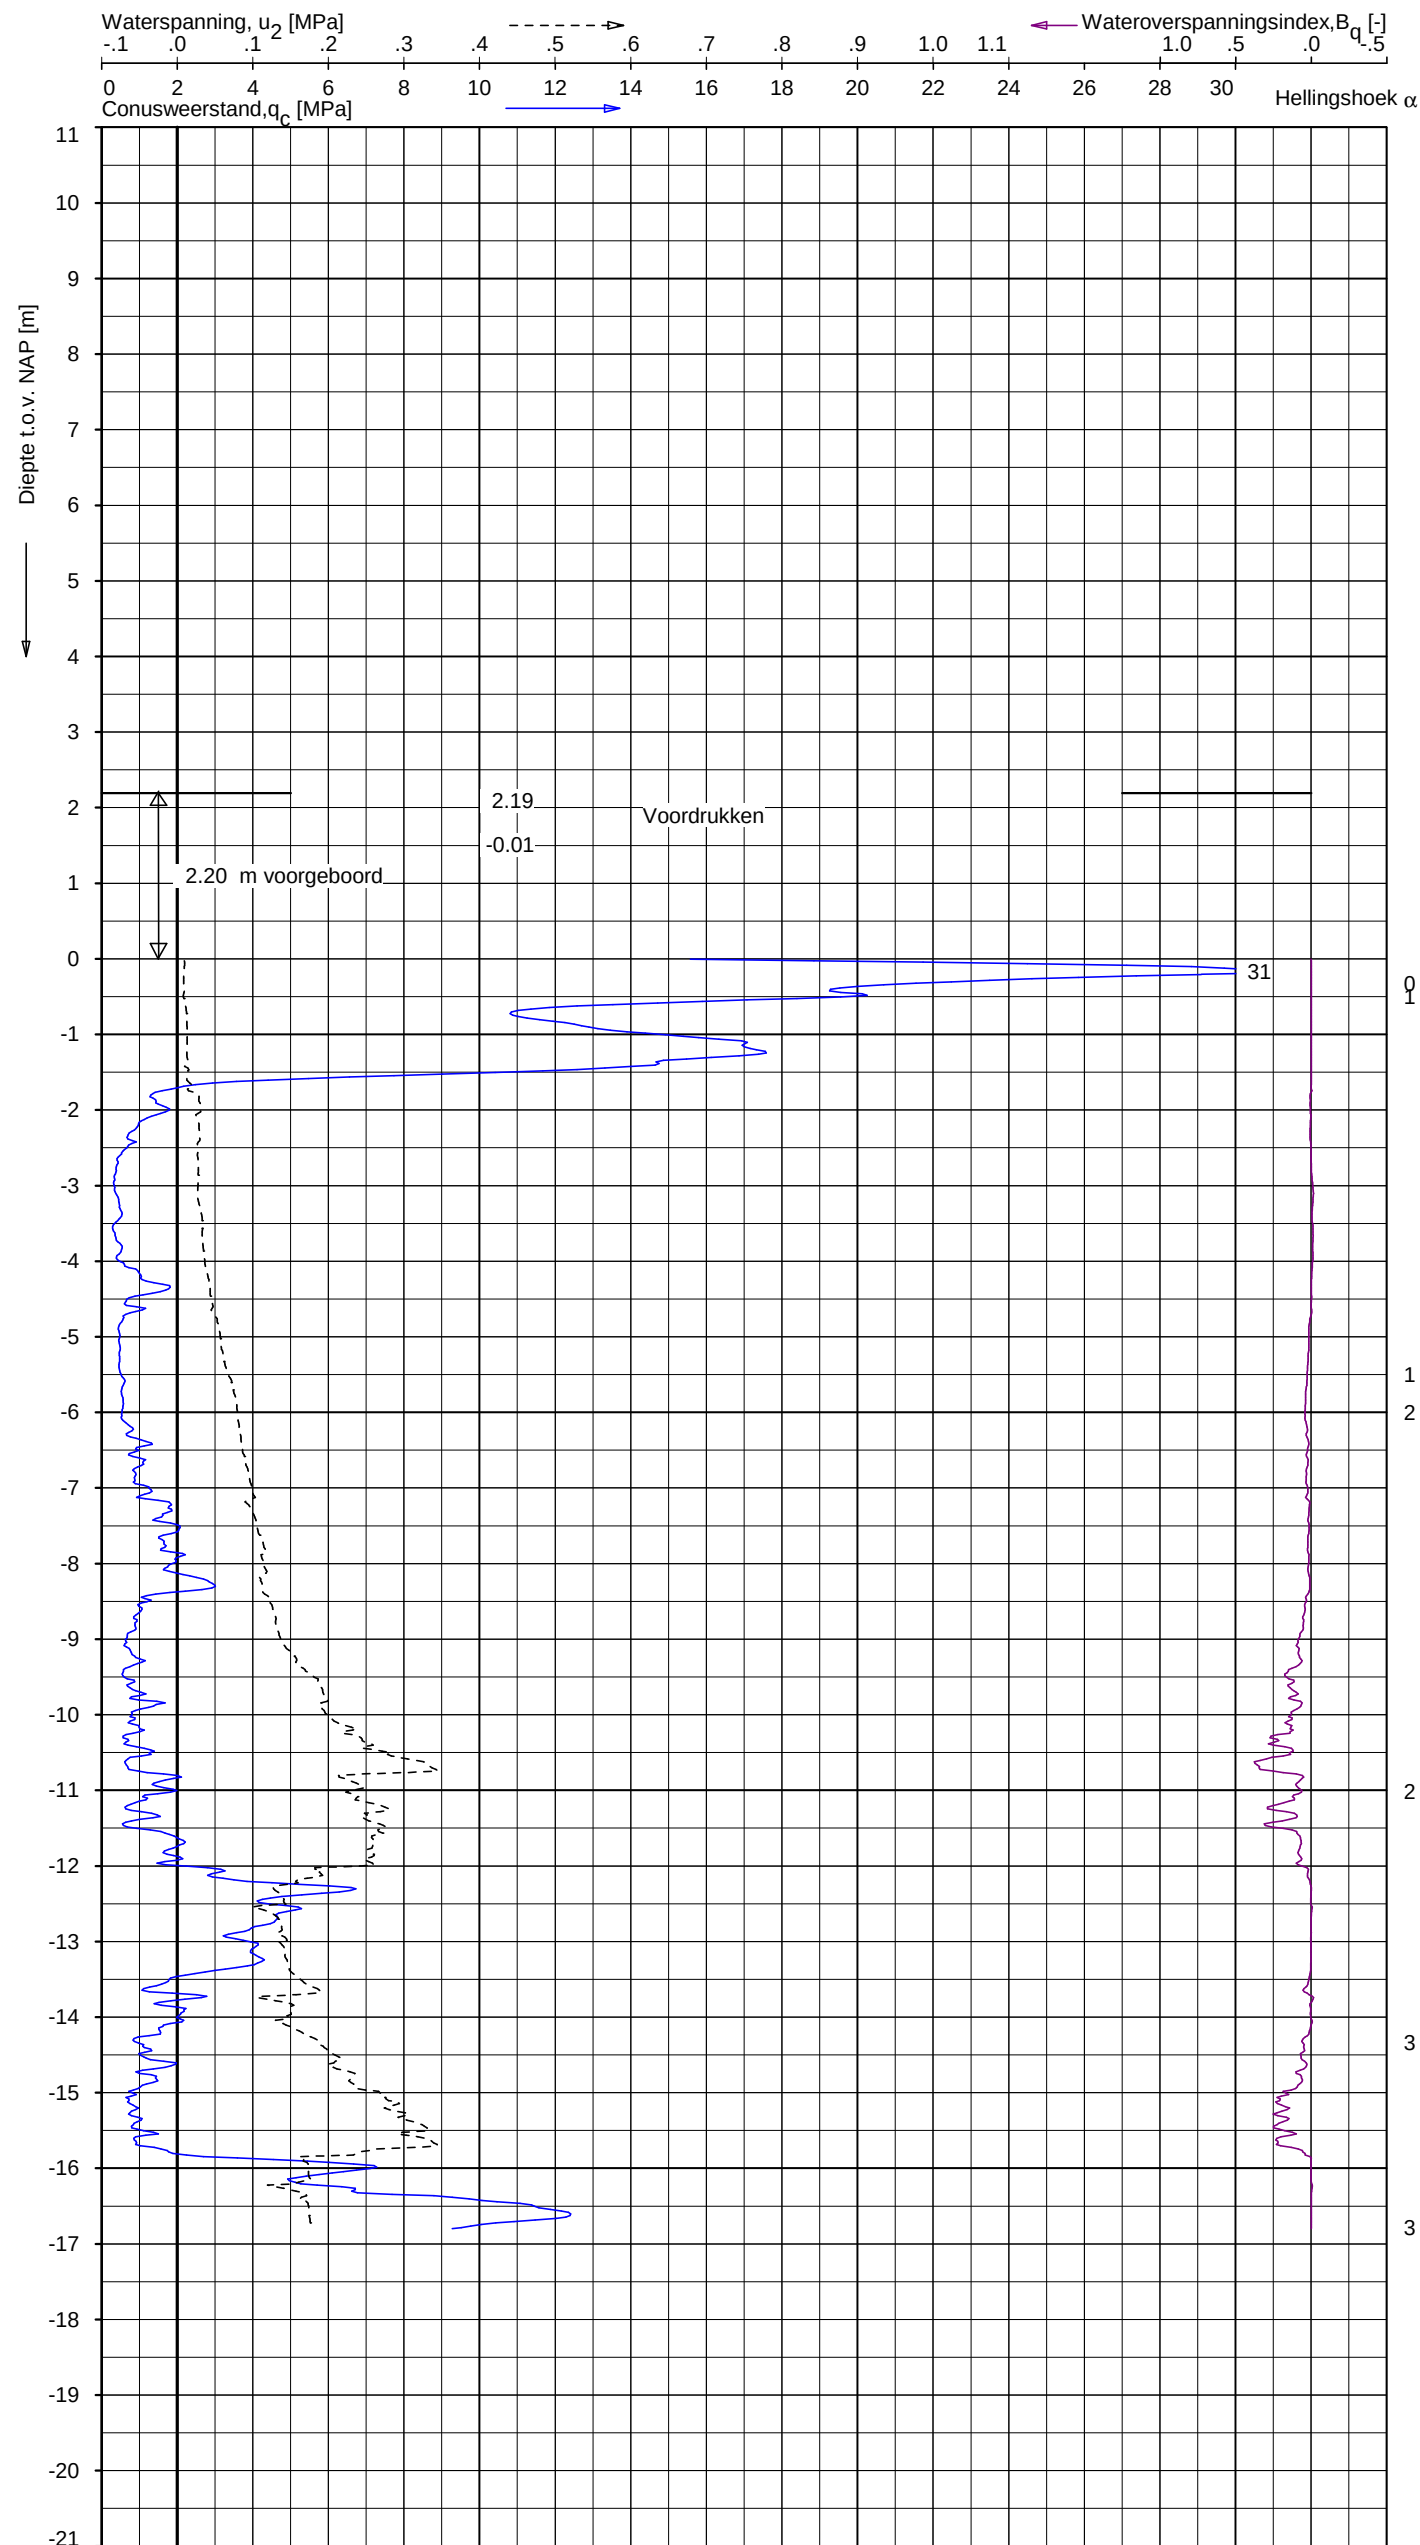

Indicatieve bodembeschrijving
Automatisch gegenereerd uit data van de sondering, geldig onder grondwaterpeil (Robertson 1990, NL corr.)

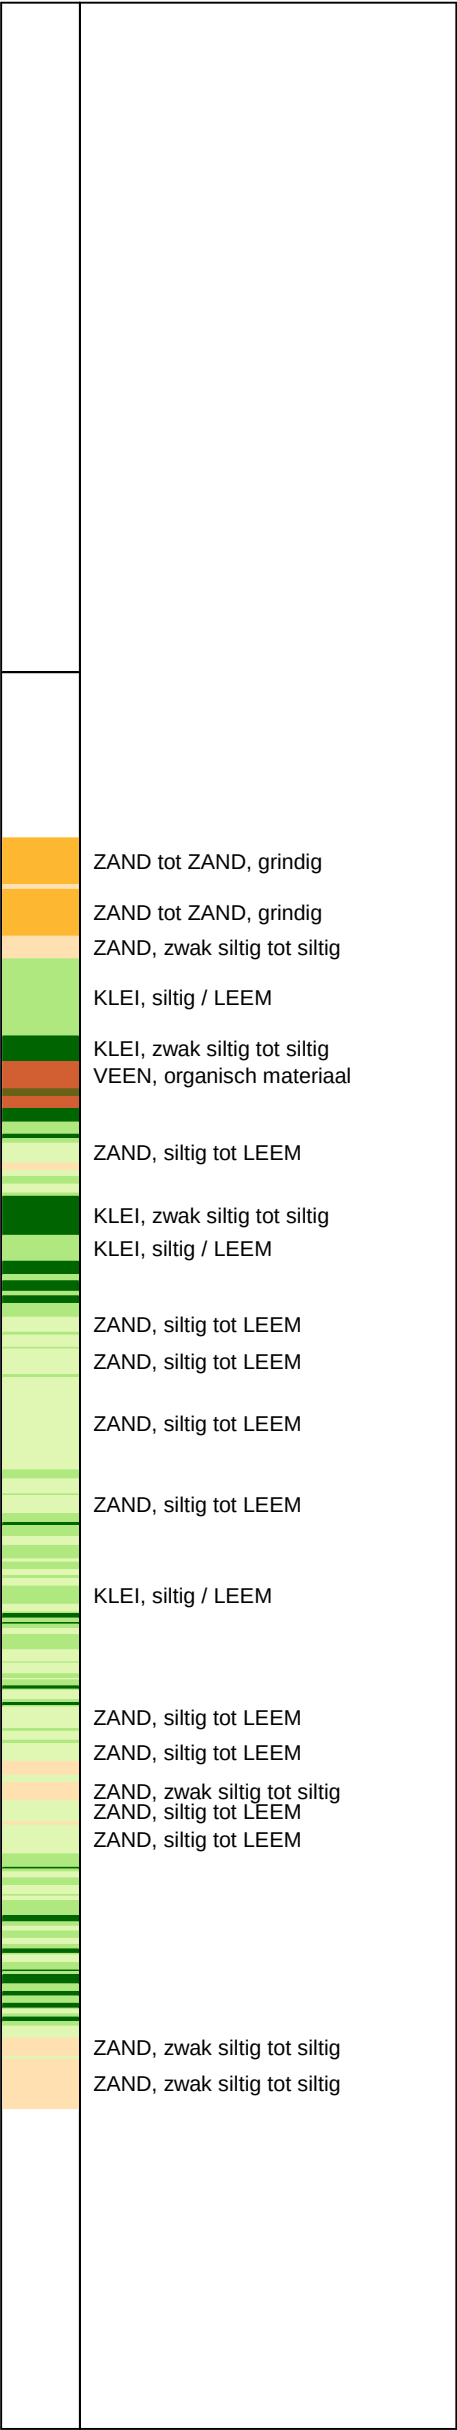

Opg.: CV/ d.d. 31-mrt-2018 Coord.: X= 60822.6 m Y= 397424.7 m Systeem: RD Sondering volgens norm NEN-EN-ISO 22476-1
Get.: U.GUMULIAUSKAITE d.d. 17-mei-2018 MV = NAP +2.19 m Conus: CP15-CF75PB1SN2 1701-2571 Toepassingsklasse 2. Test type TE2
Conustype: $A_c = 1510 \text{ mm}^2$; $A_s = 19895 \text{ mm}^2$

SONDERING MET WATERSPANNINGSMETING

THOLEN-1 (24U)

Opdr. 1316-0342-006
Sond. 941.0-BIT-DKMP55