




Indicatieve bodembeschrijving
Automatisch gegenereerd uit data
van de sondering, geldig onder
grondwaterpeil (Robertson 1990, NL corr.)

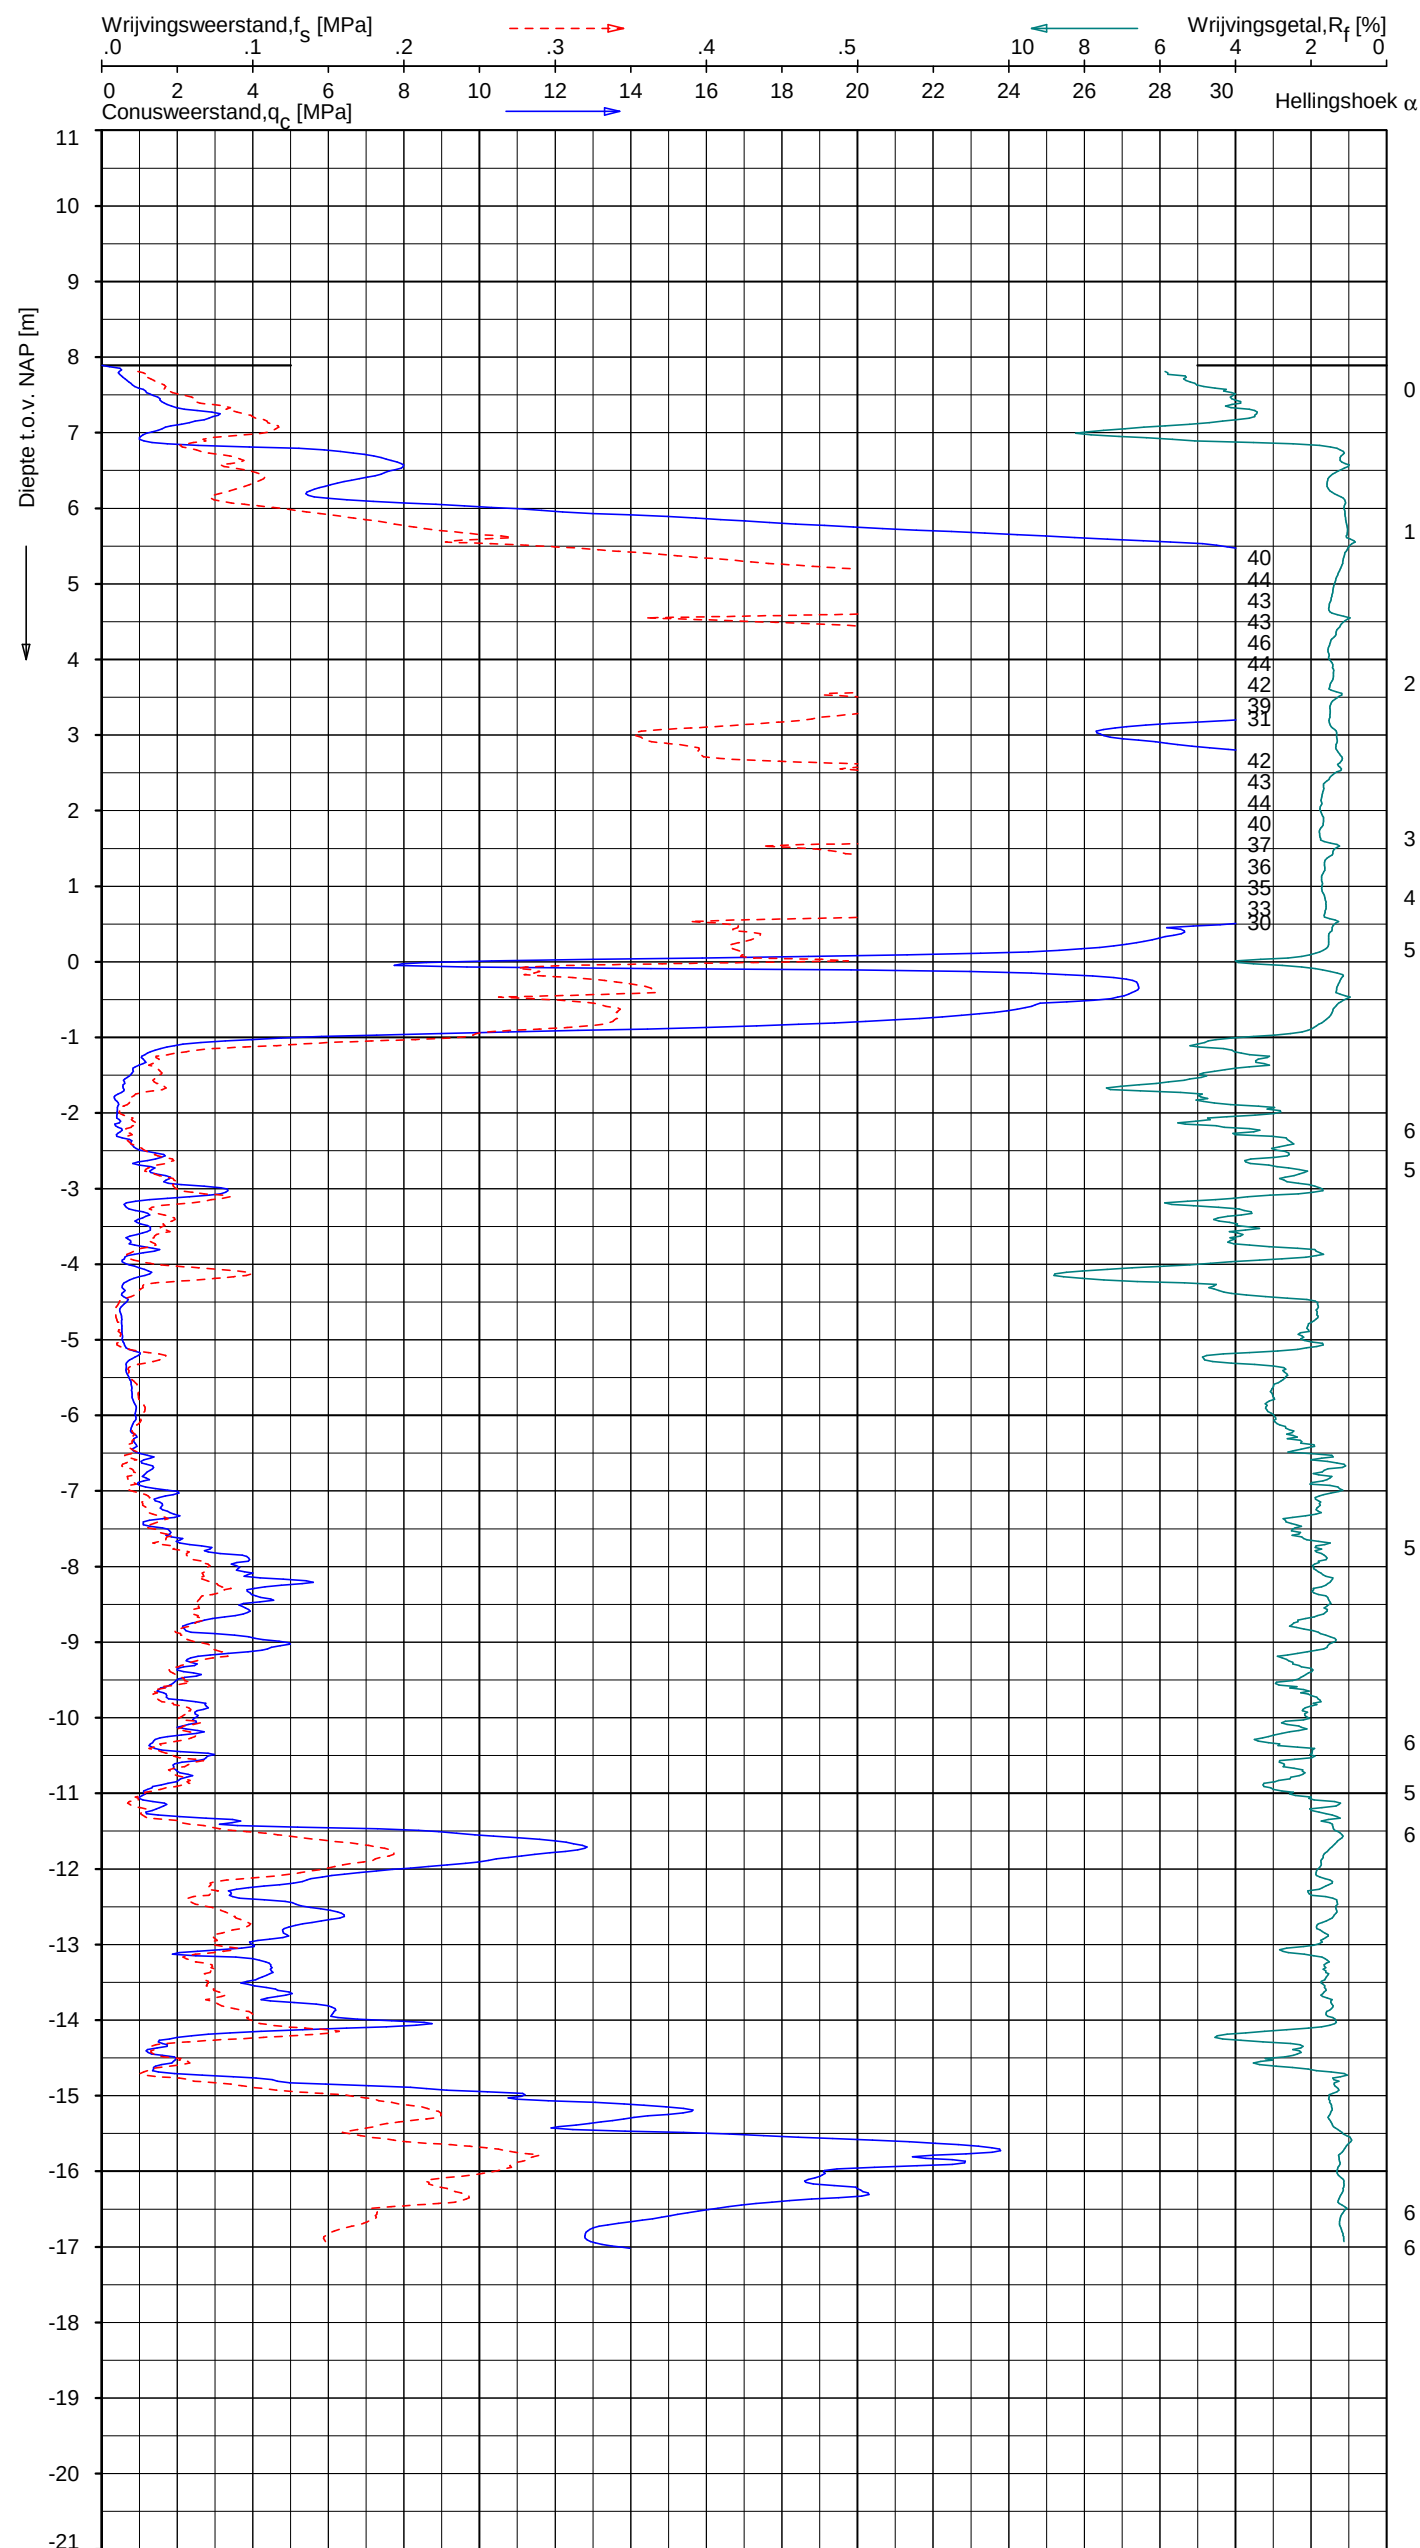

Opg.: CV/ d.d. 19-mrt-2018 Coord.: X= 60797.0 m Y= 397430.3 m Systeem: RD Sondering volgens norm NEN-EN-ISO 22476-1
Get.: U.GUMULIAUSKAITE d.d. 17-mei-2018 MV = NAP +7.89 m Conus: CP15-CF75SN2 1701-2352 Toepassingsklasse 2. Test type TE1
Conus type: $A_c = 1510 \text{ mm}^2$; $A_s = 19895 \text{ mm}^2$

SONDERING MET PLAATSELIJKE KLEEFMETING

THOLEN-1 (24U)

Opdr. 1316-0342-006
Sond. 941.0-KR-DKM10