

Boring: 941.0-KR-B4


Veldclassificatie

Pagina 1 van 2

Peilbuis
1 2

Monsternr.

Bodembeschrijving volgens NEN 5104

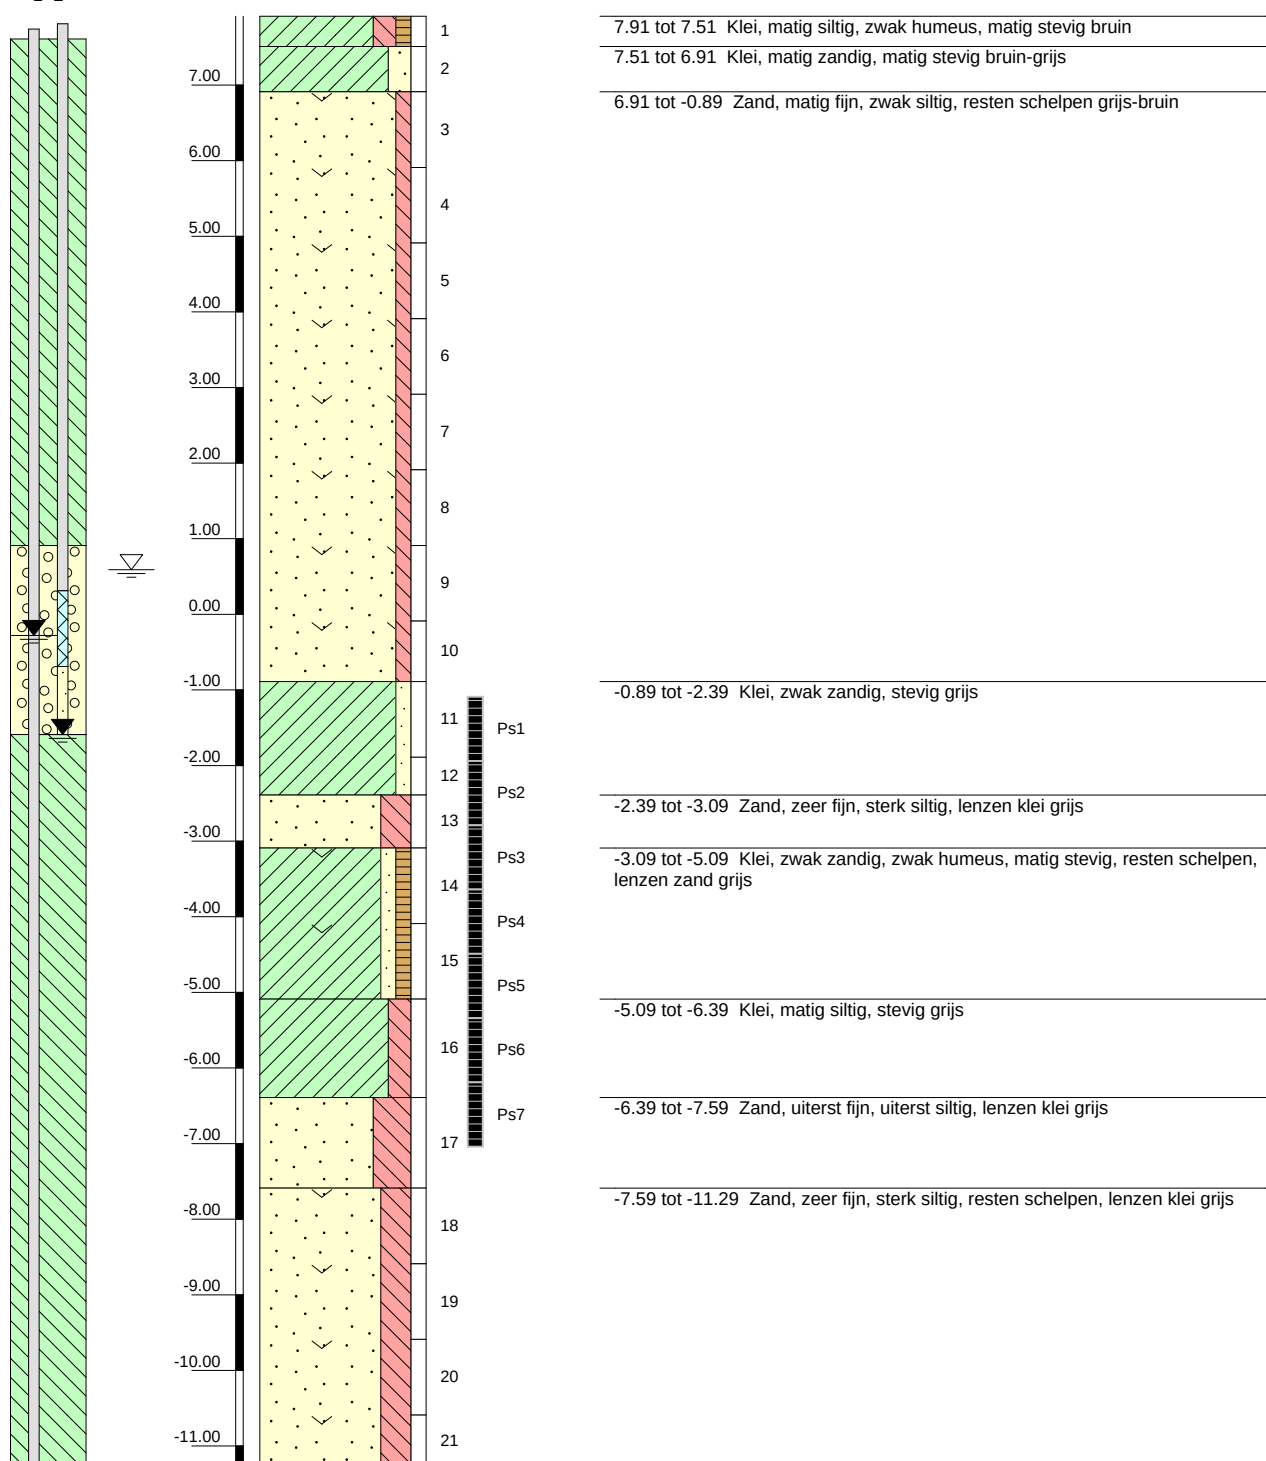

Algemene opmerking:

X: 60796.9

GWS (m tov NAP): 0.59

MV (m tov NAP): 7.91

bk PB1 (m tov NAP): 7.74

bk PB2 (m tov NAP): 7.81

bk PB3 (m tov NAP):

bk PB4 (m tov NAP):

Boorvloestof:

WS PB1 (m tov NAP): -0.28

WS PB2 (m tov NAP): -1.59

WS PB3 (m tov NAP):

WS PB4 (m tov NAP):

Datum uitvoering: 30-04-2018

Boormeester: jvk

Geclassificeerd door: jvk

BORING VOLGENS NEN-EN-ISO 22475-1


Tholen-1 (24U)

1316-0342-006

Boring: 941.0-KR-B4

Veldclassificatie

Pagina 2 van 2

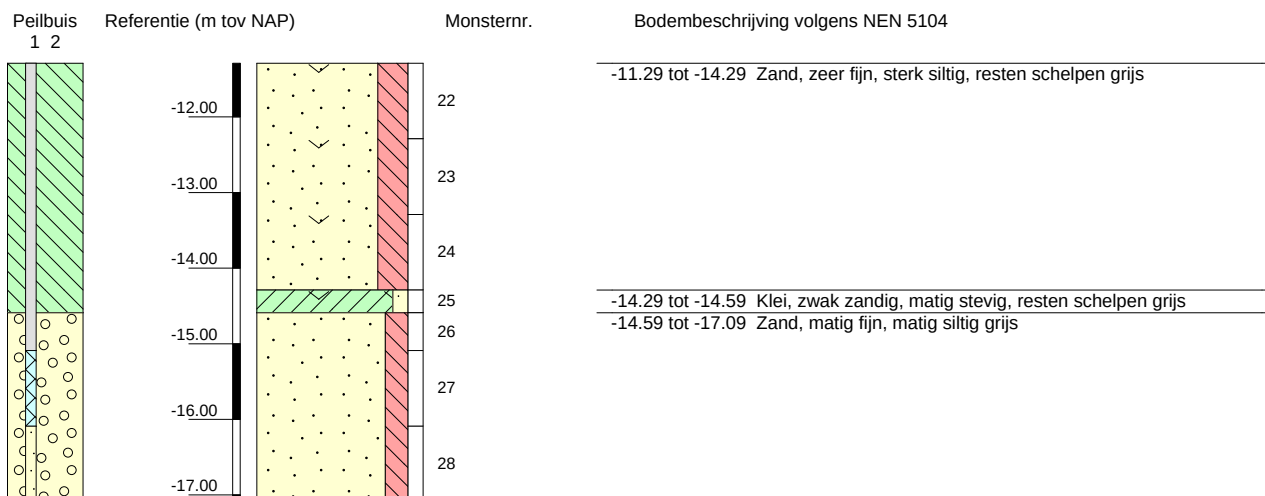

Algemene opmerking:

X: 60796.9

Y: 397430.8

Coördinatenstelsel: RD

GWS (m tov NAP): 0.59

GHG (m tov NAP):

GLG (m tov NAP):

MV (m tov NAP): 7.91

bk PB1 (m tov NAP): 7.74

bk PB2 (m tov NAP): 7.81

bk PB3 (m tov NAP):

bk PB4 (m tov NAP):

Boorvloeistof:

WS PB1 (m tov NAP): -0.28

WS PB2 (m tov NAP): -1.59

WS PB3 (m tov NAP):

WS PB4 (m tov NAP):

Datum uitvoering: 30-04-2018

Boormeester: jvk

Geclassificeerd door: jvk

BORING VOLGENS NEN-EN-ISO 22475-1

Tholen-1 (24U)

1316-0342-006